

POLITECNICO DI MILANO
SCUOLA DEL DESIGN
C.L. DESIGN DEGLI INTERNI
PROGETTO:

Cassettiera KULLEN no. 803.092.41

CORSO:
STRUMENTI E METODI
DEL PROGETTO

DOCENTE:

MARCO FERRARA

ARIANNA PERRONE

STUDENTI:

ABACO DEI COMPONENTI

NOTE:

NOME FILE:
KULLEN_ 803-092-41.dwg

VERS [


A YYYY.MM.DD

TAVOLA NO.: 000 DI 999

. . .

A701

DATA: **2017/05/22** SCALA: **1:5** REV: **A** FORMATO: **A1**

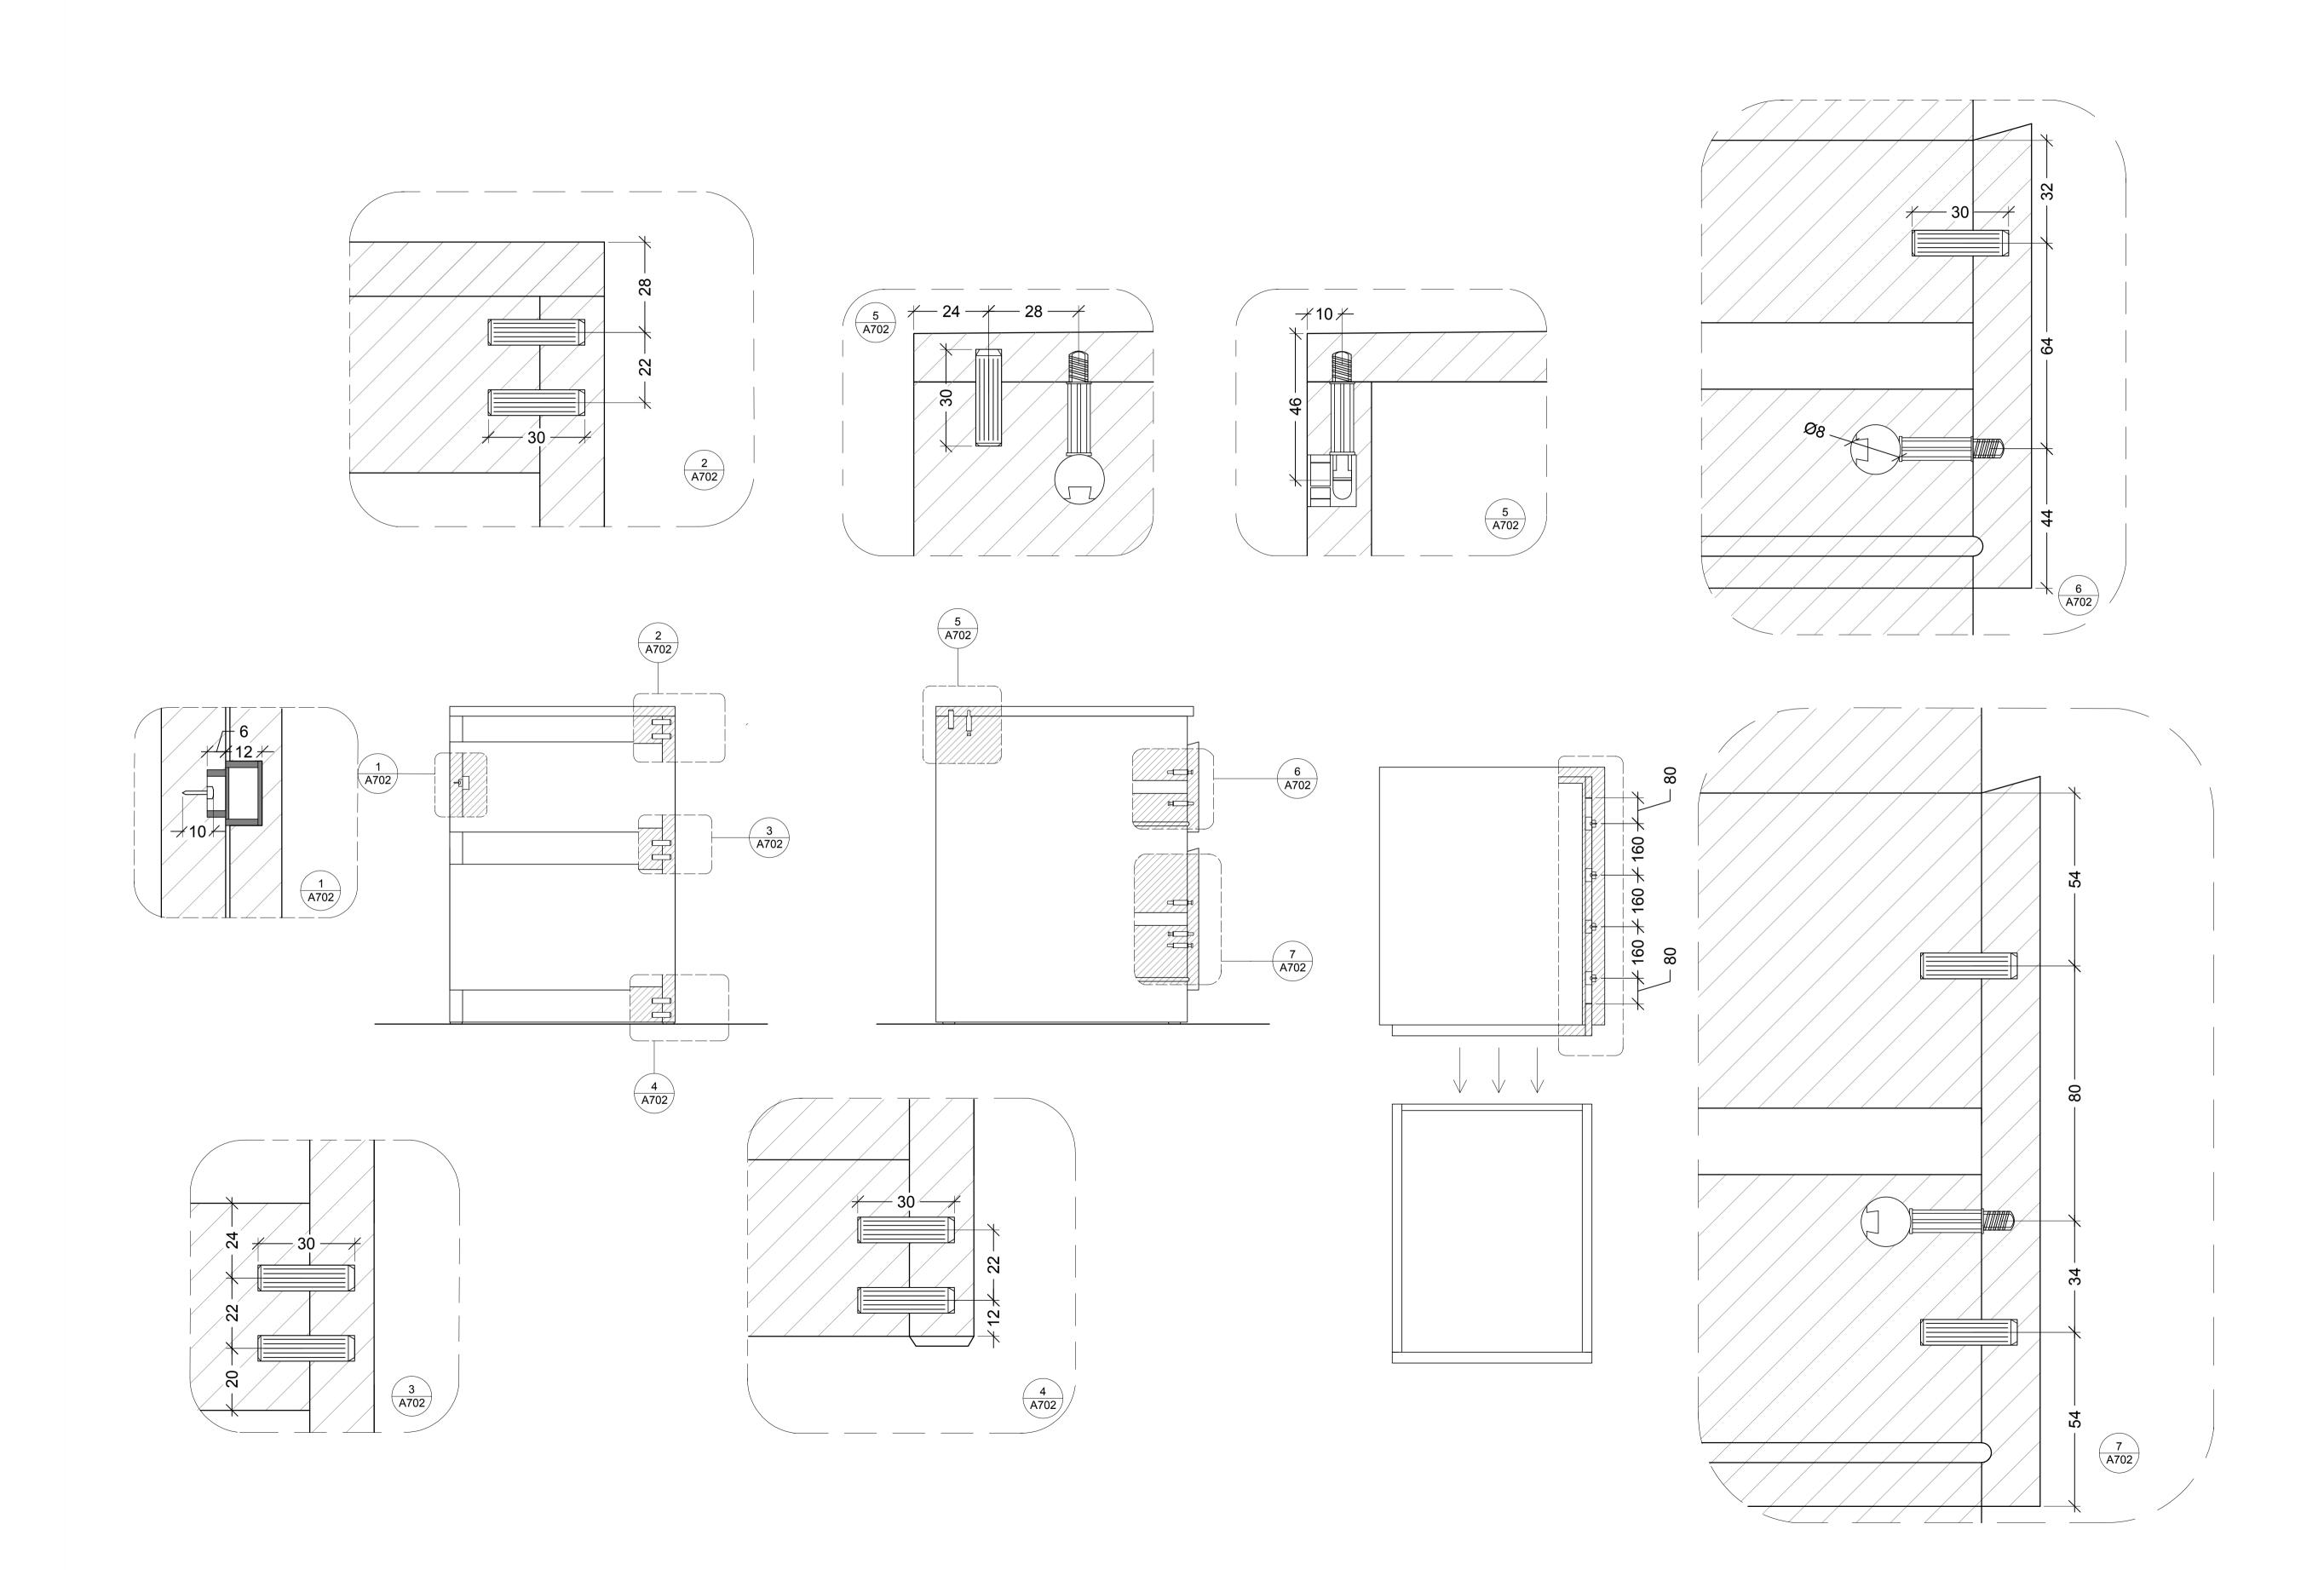

POLITECNICO DI MILANO SCUOLA DEL DESIGN C.L. DESIGN DEGLI INTERNI PROGETTO:

> Cassettiera KULLEN no. 803.092.41

> > SO:
> > STRUMENTI E METODI
> > DEL PROGETTO

DOCENTE:

MARCO FERRARA

ARIANNA PERRONE

INGRANDIMENTO DEI DETTAGLI

STUDENTI:

NOTE:

CASSETTIERA IN PROIEZINE
SC. 1:5

SC. 1:5

KULLEN_ 803-092-41.dwg

A702

TAVOLA NO.:

YYYY.MM.DD 000 DI 999

DATA: **2017/05/22** SCALA: **1:1** REV: **A** FORMATO: **A1**