

POLITECNICO DI MILANO
SCUOLA DEL DESIGN
C.L. DESIGN DEGLI INTERNI
PROGETTO:

Cassettiera **KULLEN** no. 803.092.41

STRUMENTI E METODI DEL PROGETTO DOCENTE: MARCO FERRARA

STUDENTI: ARIANNA PERRONE

INGRANDIMENTO DEI DETTAGLI


KULLEN\_ 803-092-41.dwg

YYYY.MM.DD 000 DI 999

TAVOLA NO.:

A702

DATA: 2017/05/22 SCALA: 1:5
REV: A FORMATO: A1

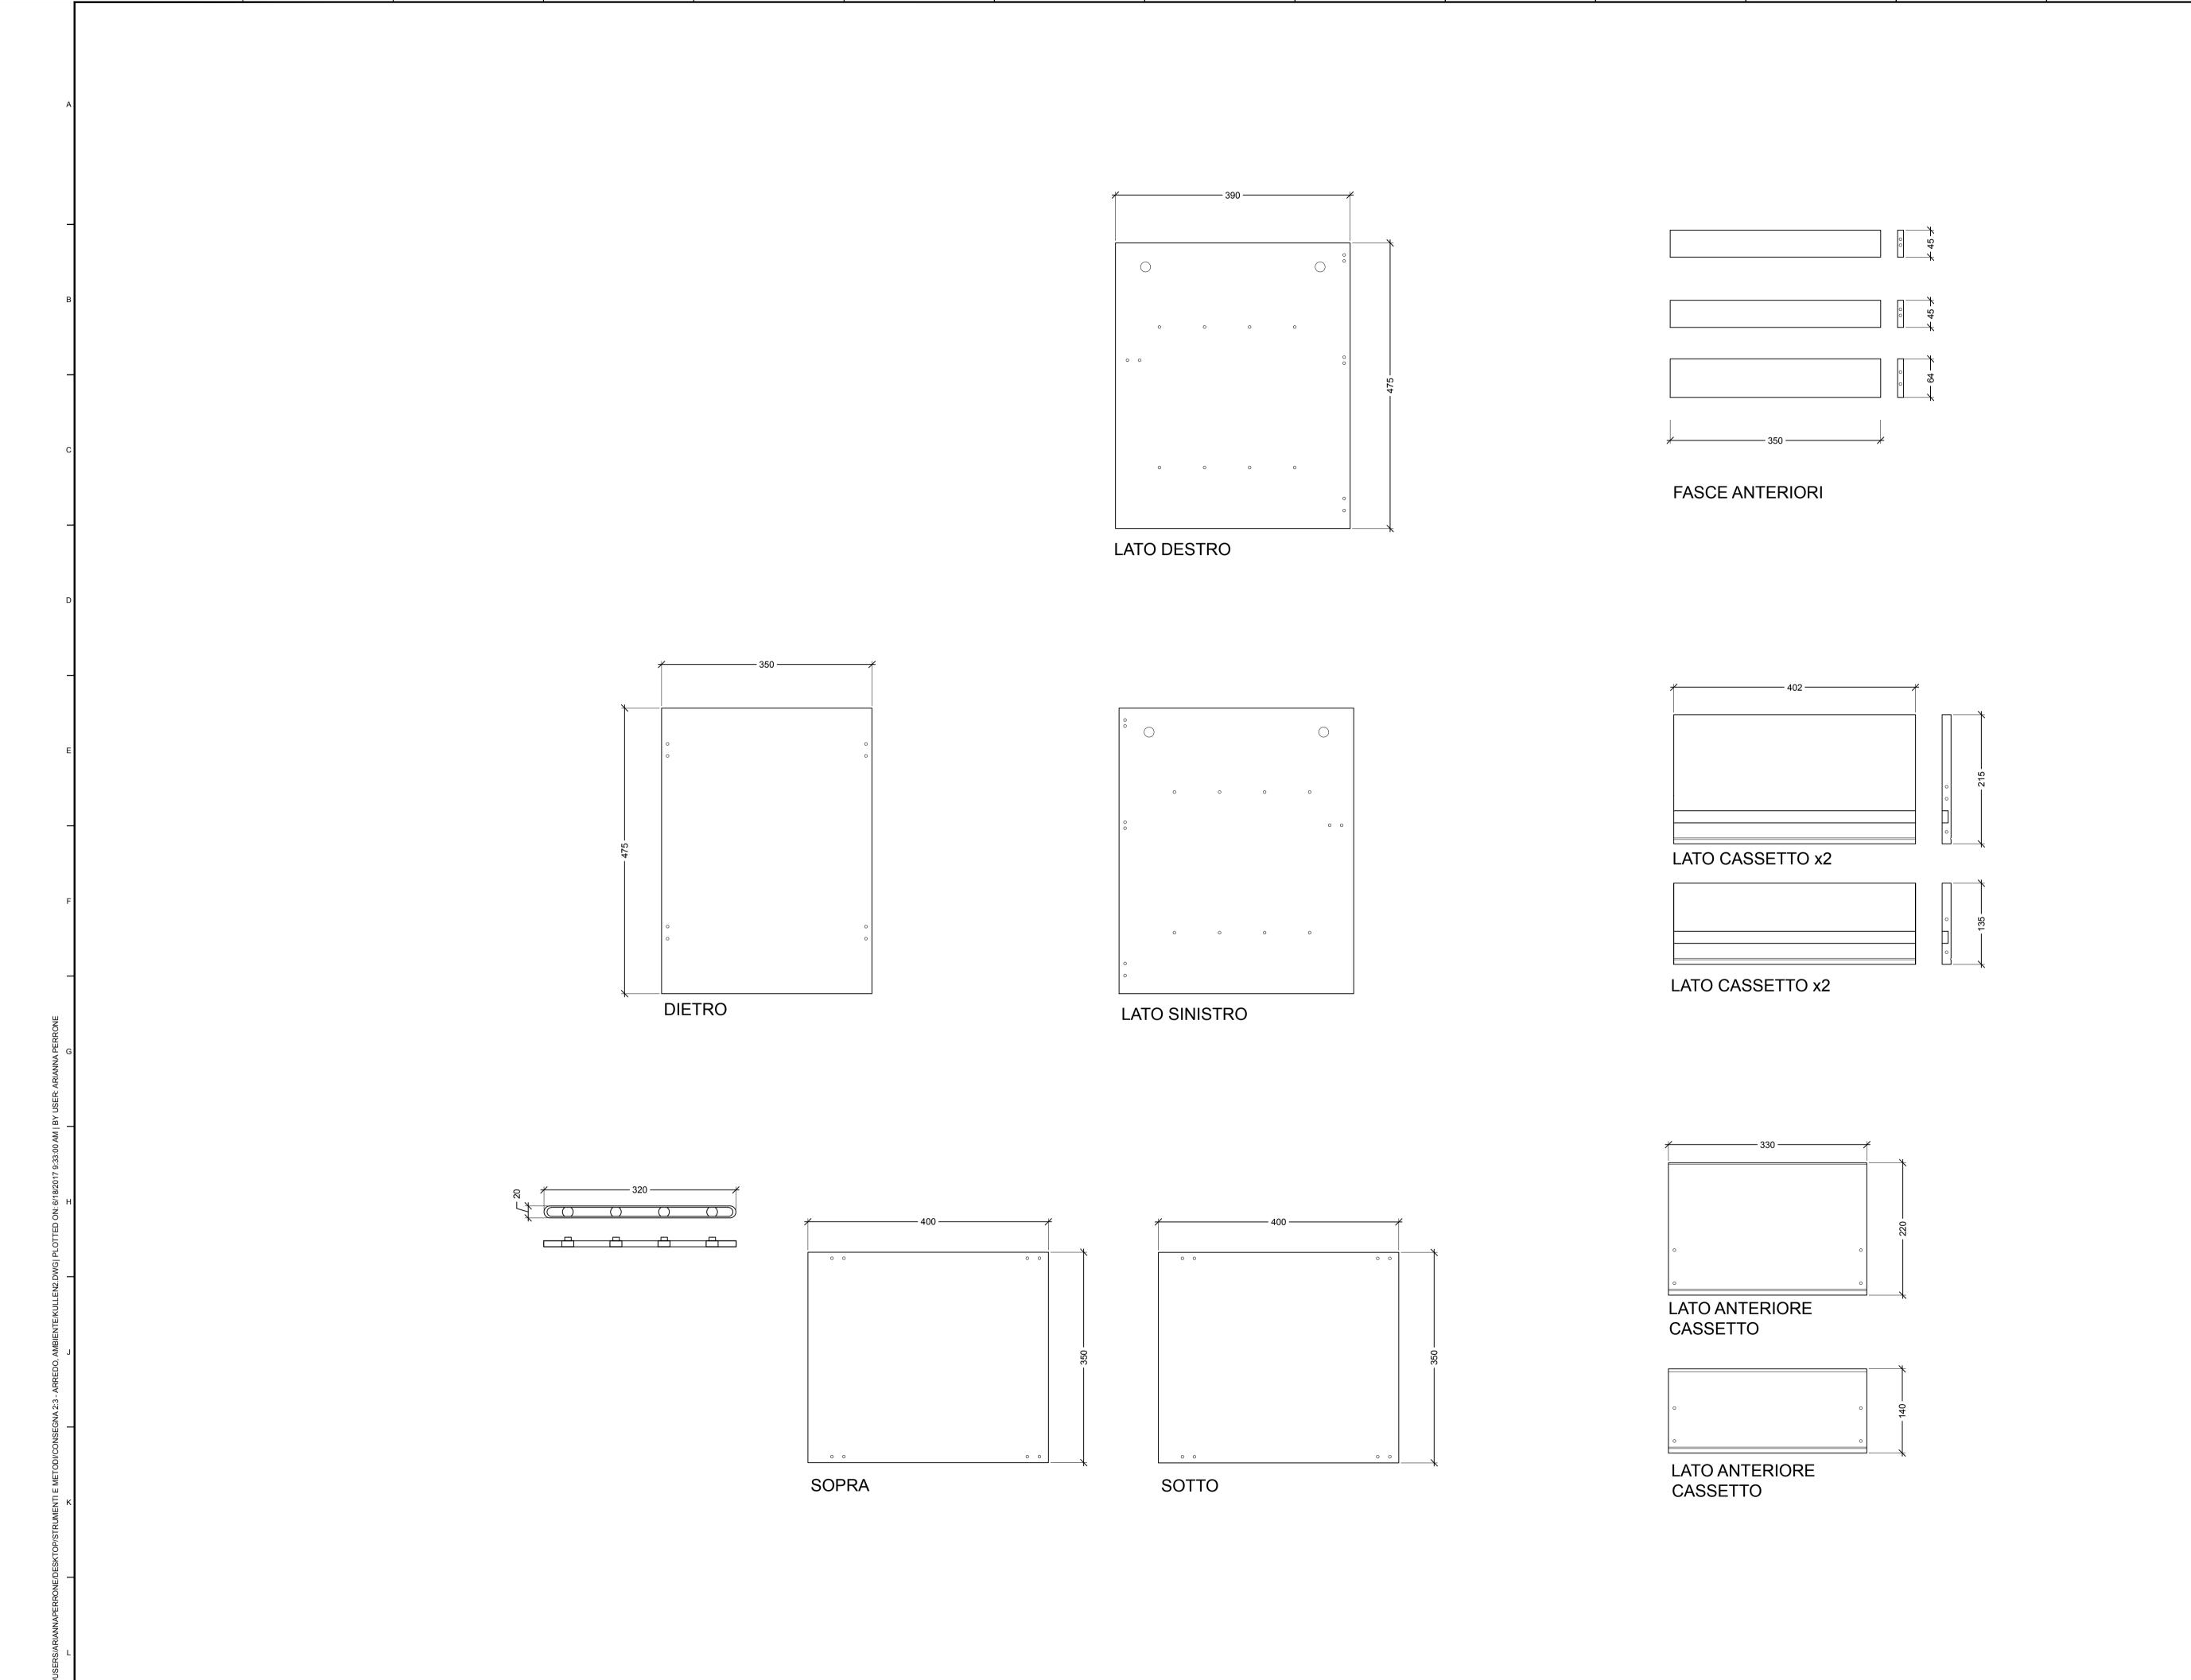



Cassettiera KULLEN no. 803.092.41

CORSO: STRUMENTI E METODI DEL PROGETTO
DOCENTE:

STUDENTI:

ARIANNA PERRONE

OGGETTO:

NOTE:

NOME FILE:
KULLEN\_ 803-092-41.dwg

VERS [

A YYYY.MM.DD

TAVOLA NO.: 000 DI 999

A 704

A701

DATA: **2017/05/22** SCALA: **1:5** REV: **A** FORMATO: **A1**