174


160

SPALLIERA

160

197

LATO X2

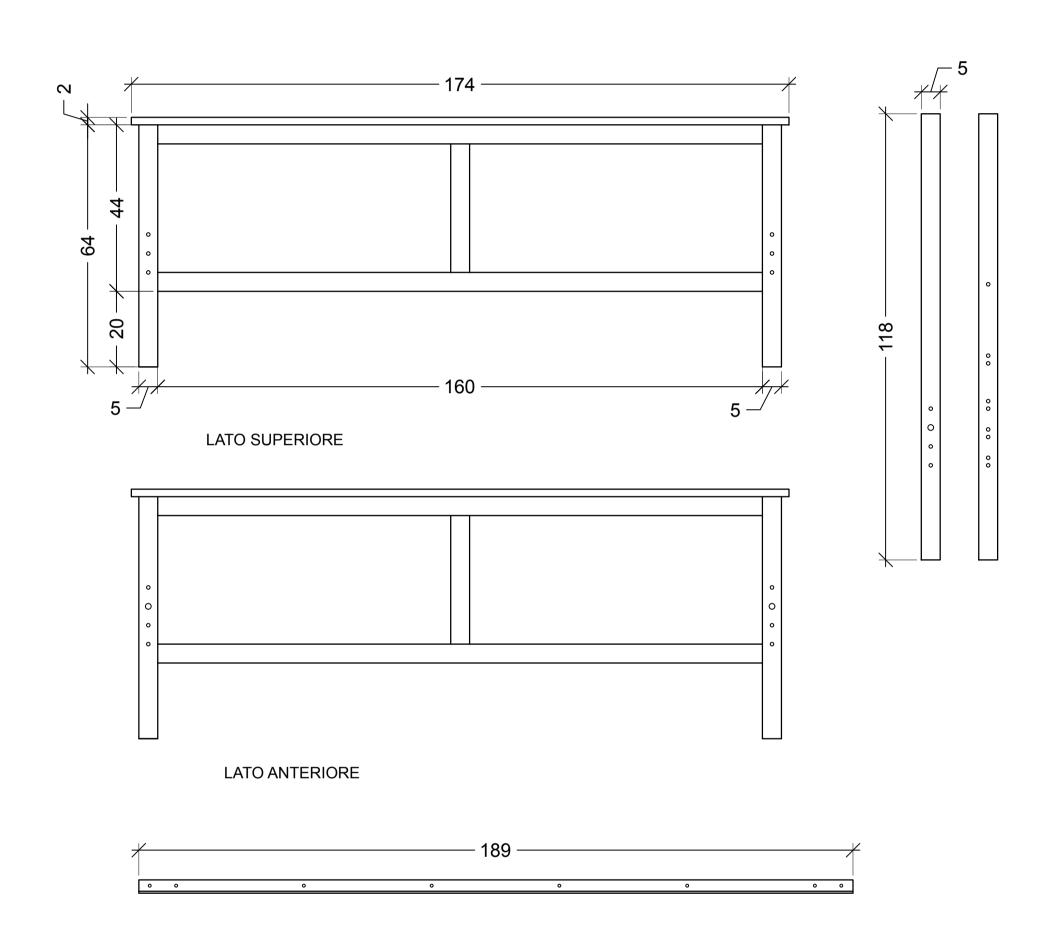

*tutti i pezzi sono realizzati in pino massiccio , mordente e vernice acrilica

POLITECNICO DI MILANO SCUOLA DEL DESIGN C.L. DESIGN DEGLI INTERNI

Letto HEMNES no. 599.293.37

ORSO:
STRUMENTI E METODI
DEL PROGETTO

MARCO FERRARA
STUDENTI:

DOCENTE:

ARIANNA PERRONE

ABACO DEI COMPONENTI

NOTE:

NOME FILE:

VERS L


HEMNES_599-293-37.dwg


A YYYY.MM.DD


TAVOLA NO.: 000 DI 999

A701

DATA: **2017/05/22** SCALA: **1:10** REV: **A** FORMATO: **A1**

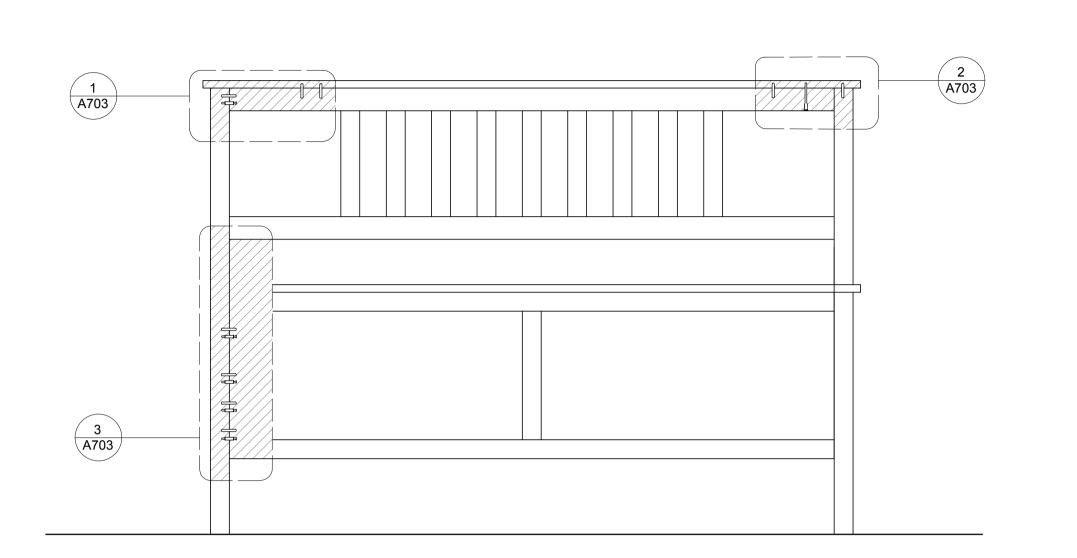

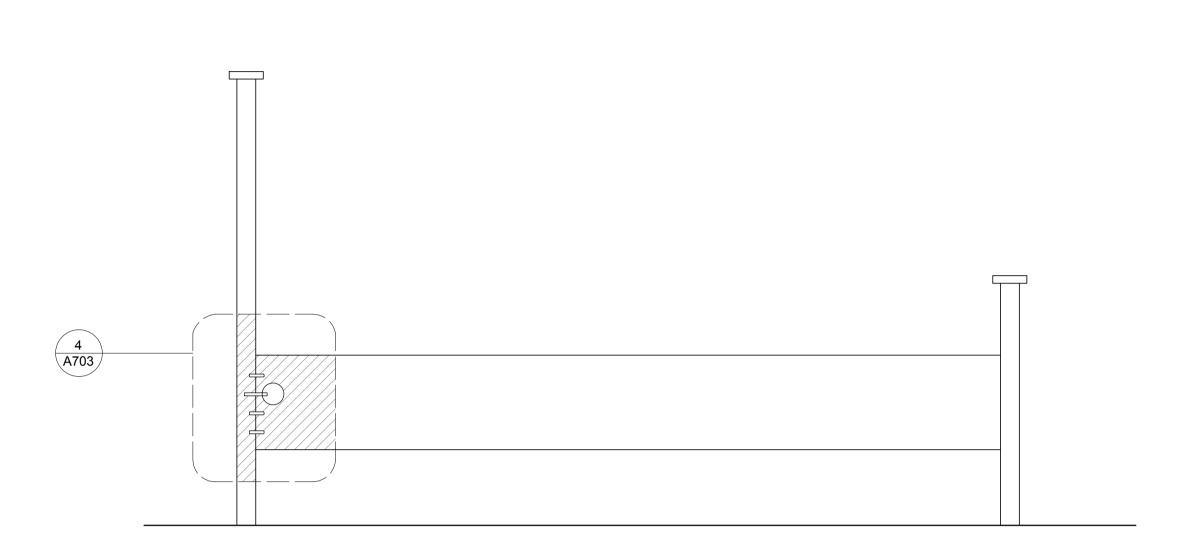

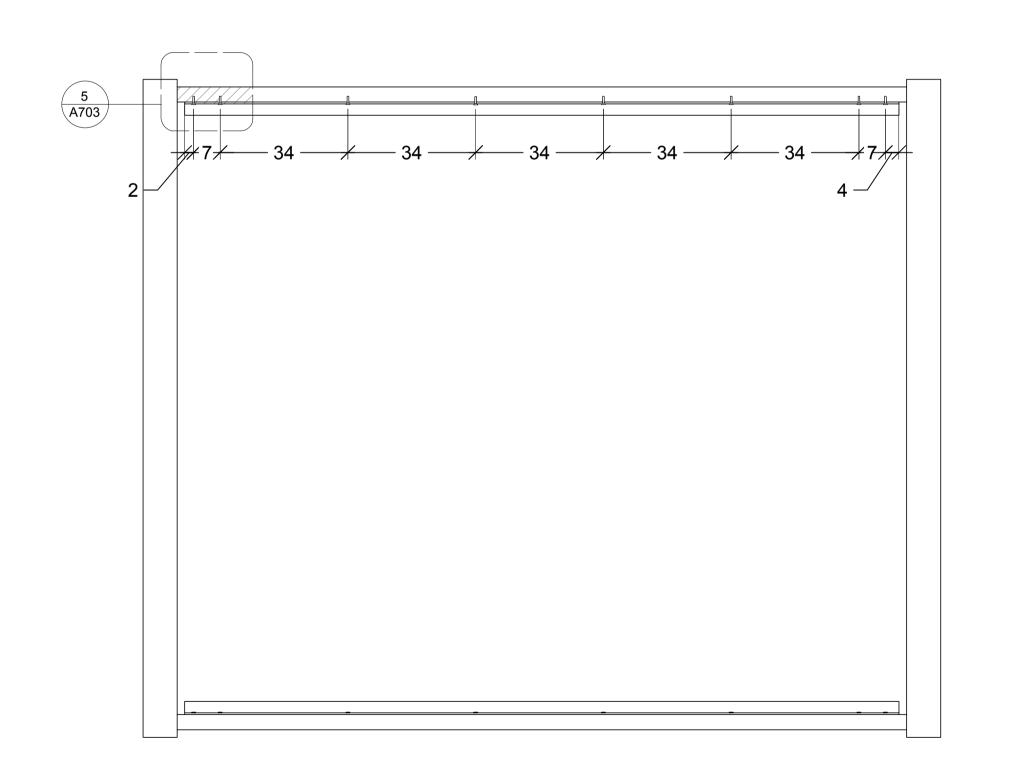

POLITECNICO DI MILANO
SCUOLA DEL DESIGN
C.L. DESIGN DEGLI INTERNI
PROGETTO:

Letto HEMNES no. 599.293.37

CORSO:
STRUMENTI E METODI
DEL PROGETTO

MARCO FERRARA

STUDENTI:

ARIANNA PERRONE

DOCENTE:

OGGETTO:

DETTAGLI DEL
MONTAGGO

NOTE:

NOME FILE:
HEMNES_599-293-37.dwg


VERS D


A YYYY.MM.DD


TAVOLA NO.: 000 DI 999


A702

DATA: **2017/05/22** SCALA: **1:10** REV: **A** FORMATO: **A1**

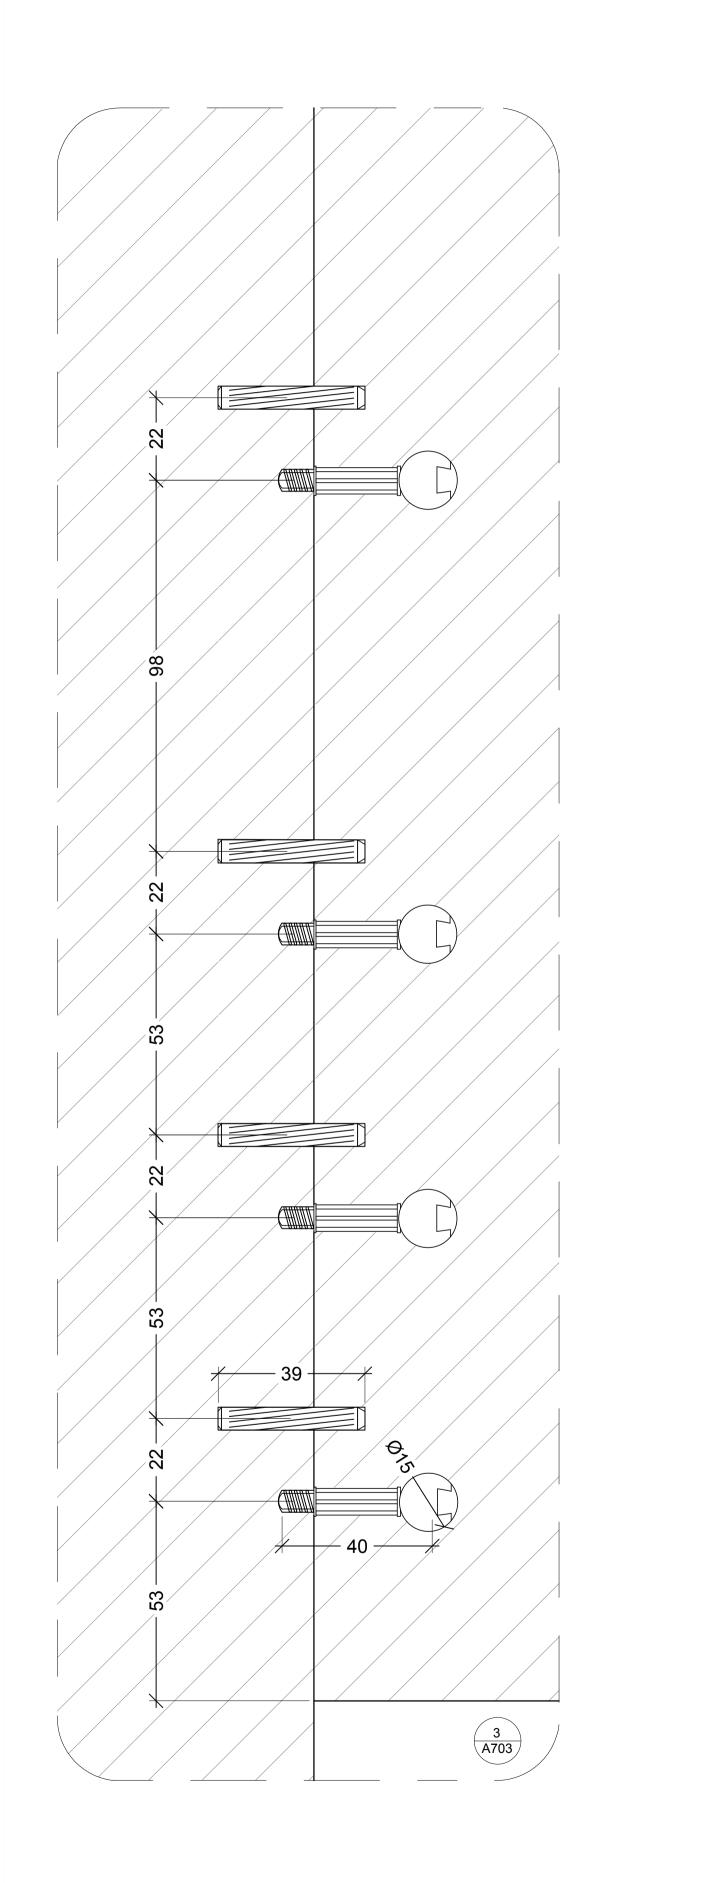

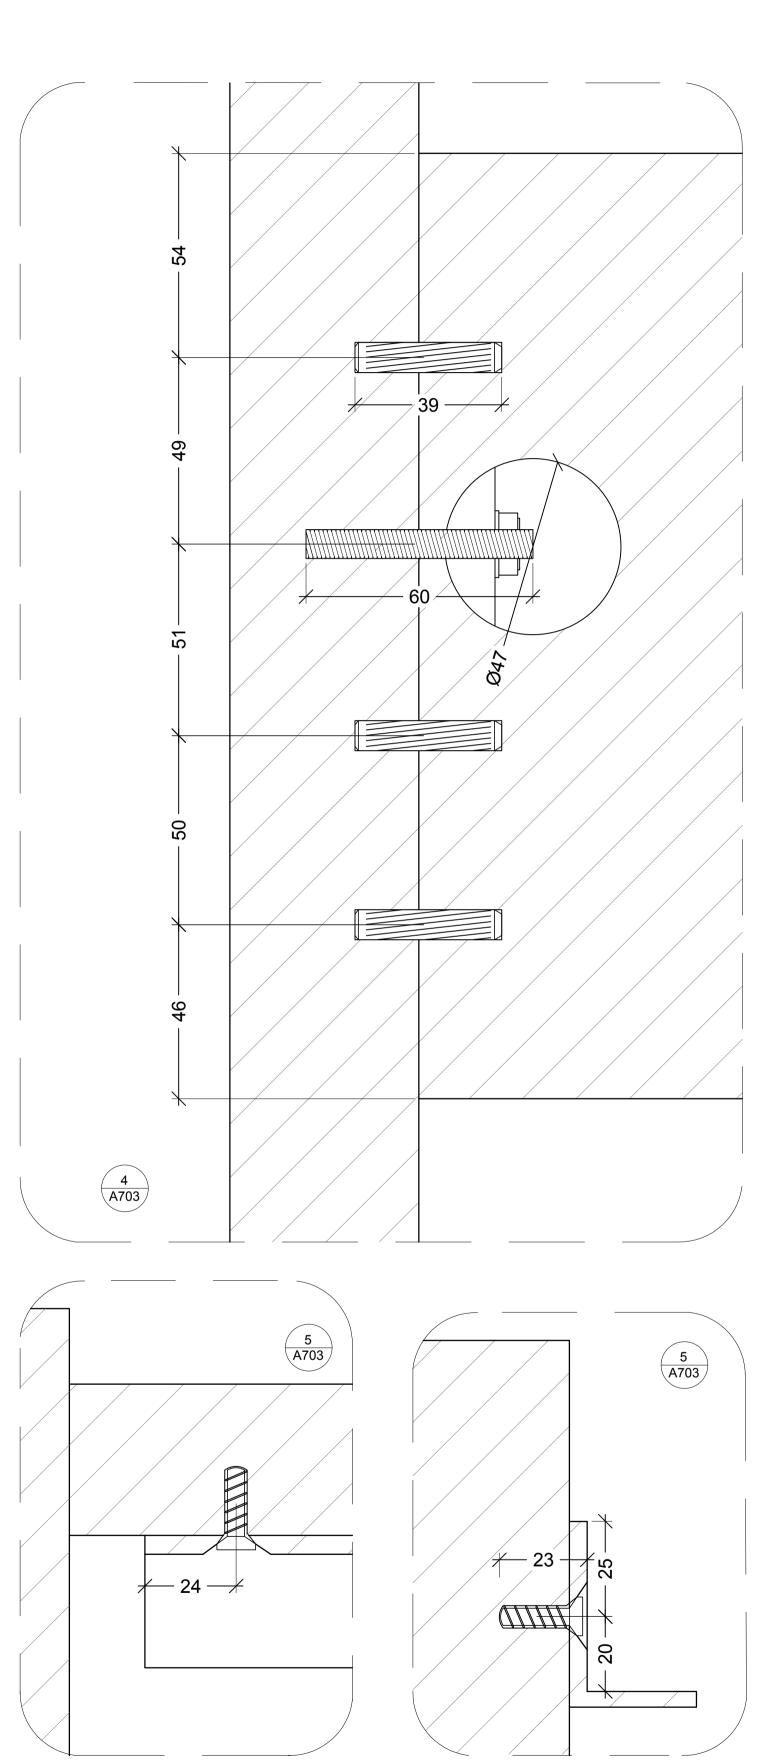

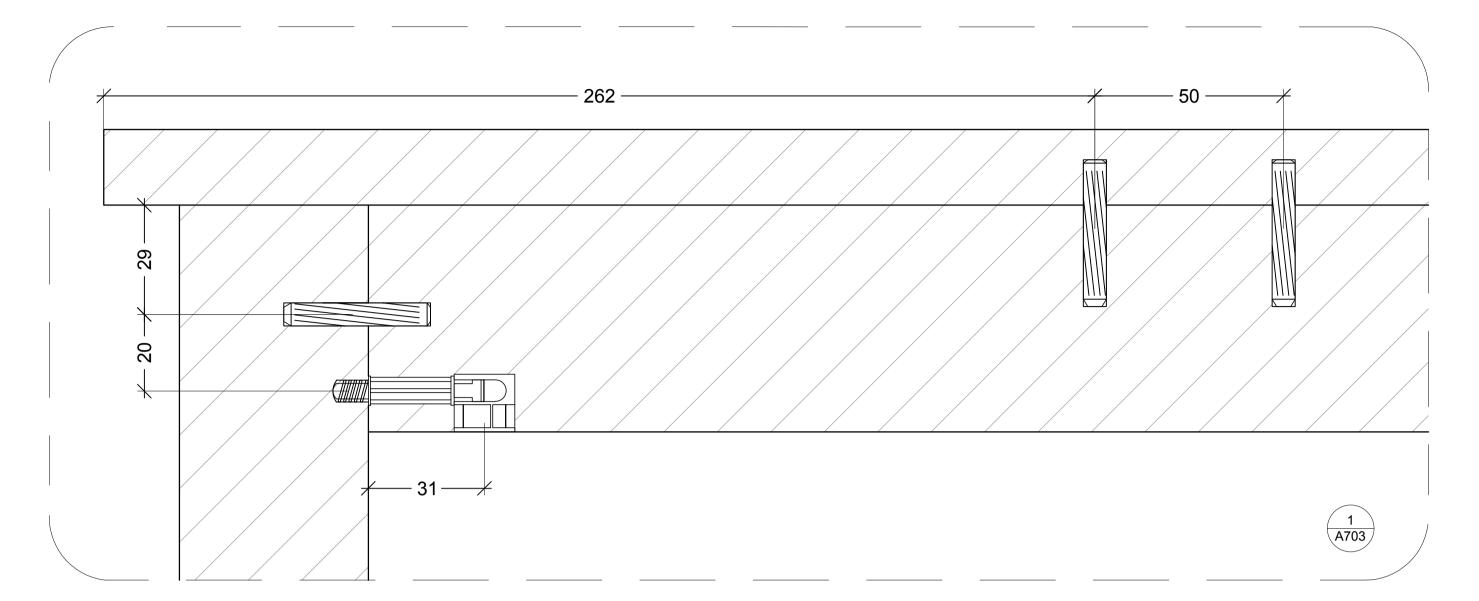

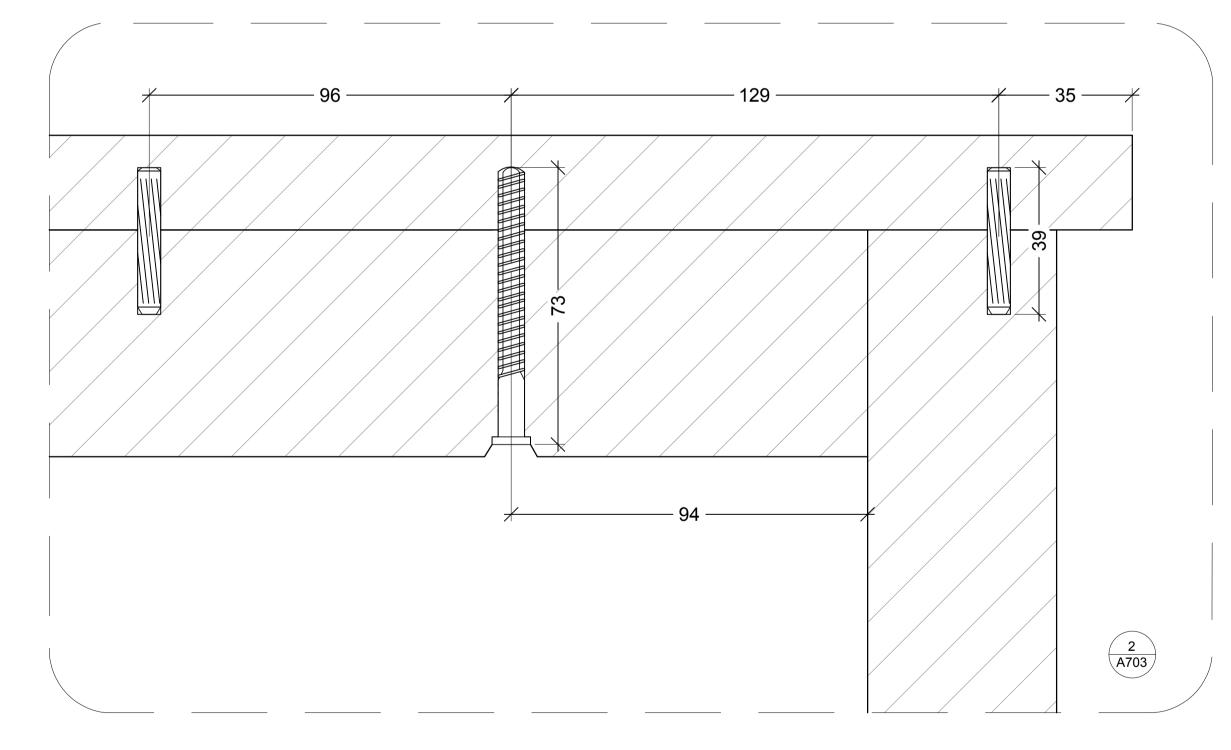

POLITECNICO DI MILANO
SCUOLA DEL DESIGN
C.L. DESIGN DEGLI INTERNI
PROGETTO:

Letto HEMNES no. 599.293.37

STRUMENTI E METODI
DEL PROGETTO

DOCENTE:

MARCO FERRARA

STUDENTI:

ARIANNA PERRONE

OGGETTO:

DETTAGLI DEL MONTAGGIO

NOTE:

NOME FILE:
HEMNES_599-293-37.dwg

VERS DATA

A YYYY.MM.DD
TAVOLA NO.: 000 DI 999

A703

DATA: **2017/05/22** SCALA: **1:1** REV: **A** FORMATO: **A1**